



| REVISIONS | | | |
|---|---|---|---|
| REV | DESCRIPTION | BY | DATE |
| K | R127 amendment: outer walls grown outward to 4.3, curved bend saddles back (#271) | Claude | 16/10/26 |
| M | Dan's N2 / N3 / N4 answers (#273) | Claude | 16/10/26 |
| N | LOGIC Bus 2 x 48.1 corner joint stays solid (sweep fixes) (#275); first drawing issued (#280) | Claude; drawing SteveCAD | 17/10/26 |
| P | Dan's markup 17/10/26 (23-21): spare fuse positions deleted, the rest on a 9.35 grid from y 31.7 (jumpers sized by fuse) | Claude | 18/10/26 |
| R | Fit audit + N21 18/10/26 (R165, R166): micro relay pattern to TE V23074, sockets 3.2 deep; mini fuse sockets at the real 8.1 pitch with TE MCP 2.8 receptacles; box 3.15 wider; spine 3.0 | Claude | 18/10/26 |
| S | HEAD relays M1 / M2 get the 87a blade slot (R170, #308): model changed after the R drawing; drawing reissued in the buildability review 18/10/26 | Claude | 18/10/26 |

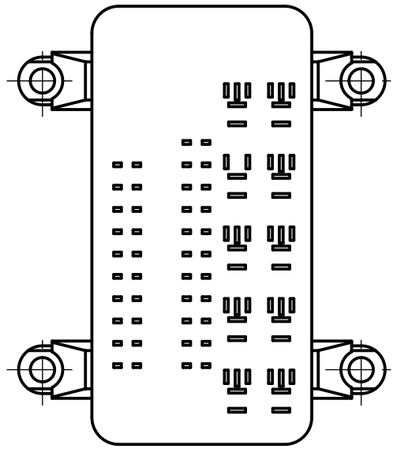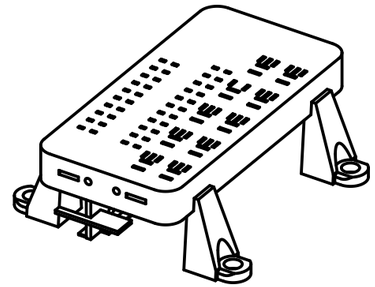

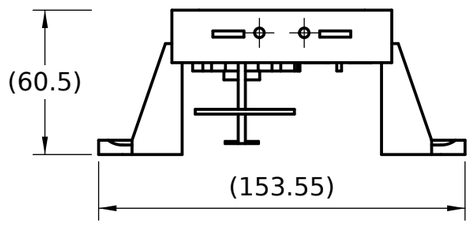

**TRIMETRIC VIEW (SCALE 1:3.33)**

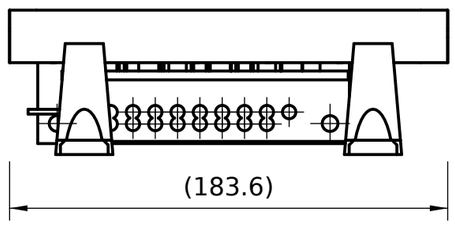


**NOTES:**

1. MATERIAL: PA12, POWDER-BED PRINTED (SLS/MJF). PRINT FROM THE STL/STEP MODEL.
2. DIMENSIONS ARE REFERENCE ONLY (OVERALL SIZE); THE 3D MODEL DEFINES ALL OTHER FEATURES.

**UNLESS OTHERWISE SPECIFIED:**
DIMENSIONS ARE IN MILLIMETERS
TOLERANCES:
X ±0.5 X.X ±0.2
X.XX ±0.05 ANGLES ±0.5°
BREAK SHARP EDGES 0.2-0.4
SURFACE FINISH Ra 3.2 µm
INTERPRET PER ASME Y14.5-2018

COMPANY / PROJECT
**ST185 CELICA GT-FOUR - LINK ECU CONVERSION**

TITLE
# LOGIC BOX - BASE

| PART / DWG NO. | REV | MATERIAL |
|---|---|---|
| **ST185-FB-105** | **S** | PA12 (SLS / MJF) |

| SCALE | UNITS | SIZE | SHEET | DATE | DRAWN |
|---|---|---|---|---|---|
| 1:2.5 | mm | B (11x17) | 1 OF 1 | 2026-10-18 | SteveCAD |

SOURCE C:\\projects\\active\\st185-link-ecu-config\\cad\\fusebox\\rev7\\Logic_Base_PA12_printed.step

3RD ANGLE