REVISIONS			
REV	DESCRIPTION	BY	DATE
A	Initial	Claude	14/10/26
B	SteveCAD audit v3 fixes ported into the source (#272); first drawing issued (#280)	Claude; drawing SteveCAD	16/10/26
C	Dan's markup 17/10/26 (23-06): battery block pad 25.4 x 3.2 x 15.5 (bar width, from the 1 in x 1/8 in strip stock), held by two snap tabs	Claude	18/10/26

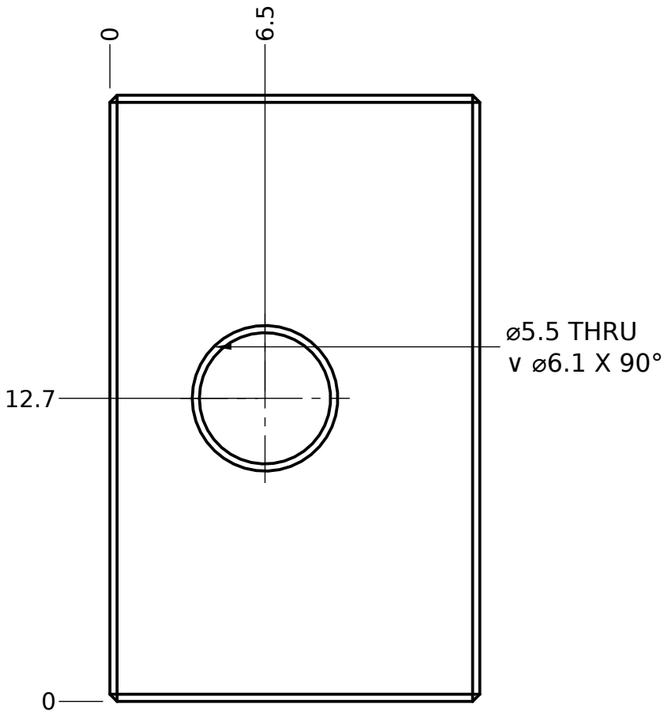

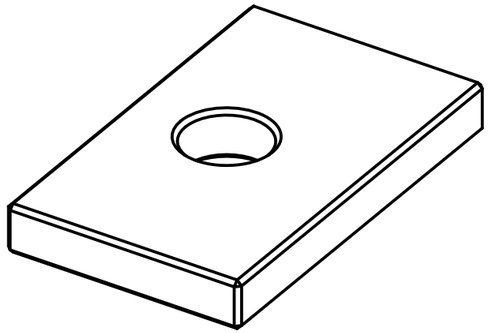

TRIMETRIC VIEW (SCALE 3:1)

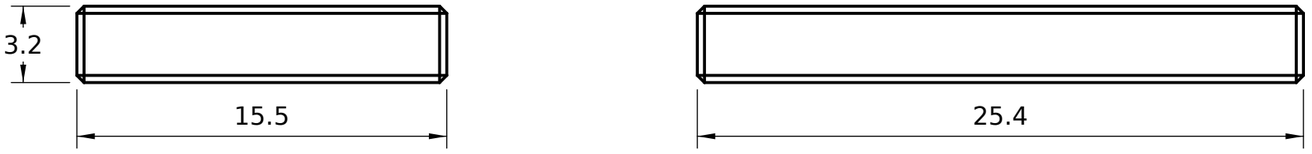

NOTES:

1. MATERIAL: C110 COPPER, TINNED. CUT FROM 1" x 1/8" (25.4 x 3.2) TINNED FLAT BAR (MECCANIXITY B0CGJC2S1L, THE SPARE BAR OF THE LOGIC STRIP PAIR). QTY 1.
2. SAW CUT, DRILL; DEBURR ALL HOLES AND EDGES. DO NOT REMOVE TIN ON CONTACT FACES.

UNLESS OTHERWISE SPECIFIED:
DIMENSIONS ARE IN MILLIMETERS
TOLERANCES:
X ±0.5 X.X ±0.2
X.XX ±0.05 ANGLES ±0.5°
BREAK SHARP EDGES 0.2-0.4
SURFACE FINISH Ra 3.2 µm
INTERPRET PER ASME Y14.5-2018

COMPANY / PROJECT
ST185 CELICA GT-FOUR - LINK ECU CONVERSION

TITLE
BATTERY BLOCK PAD 25.4 x 3.2 x 15.5

PART / DWG NO.	REV	MATERIAL
ST185-FB-112	C	C110 COPPER, TINNED

SCALE	UNITS	SIZE	SHEET	DATE	DRAWN
4:1	mm	B (11x17)	1 OF 1	2026-10-18	SteveCAD

SOURCE C:\\projects\\active\\st185-link-ecu-config\\cad\\fusebox\\rev7\\BattRelay_Pad_Out_CuC110_25p4x3p2.step

3RD ANGLE