



REVISIONS			
REV	DESCRIPTION	BY	DATE
C	Rev 6: M6 limiters, mini-fuse input jumpers, one 40 mm standoff (R85) (#190)	DG	14/10/26
D	Rev 7 option E2: AMI fuses on the POS bus bar, one POWER + bus box (#200)	DG	14/10/26
E	Rev 7 Fusion rebuild with R120-R123 (#265)	DG	15/10/26
F	R127 amendment: outer walls grown outward to 4.3, curved bend saddles back (#271); first drawing issued (#280)	DG	16/10/26
G	Dan's markup 17/10/26 (R158): 5 more cover catches (front middle, 2 each end) with R122 screws where they fit	DG	18/10/26
H	Rebuilt with fuse box rev 8 (Dan A15 b): cover over the rev 8 base and labels	DG	13/11/26

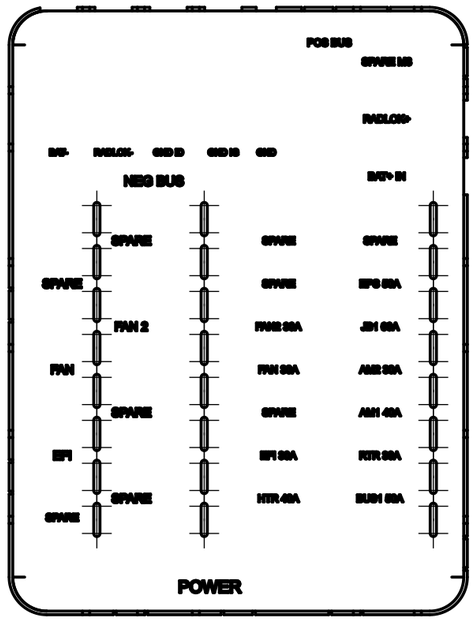

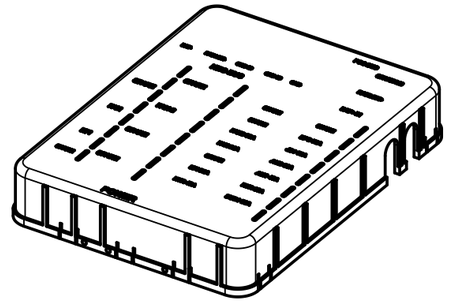

TRIMETRIC VIEW (SCALE 1:4)

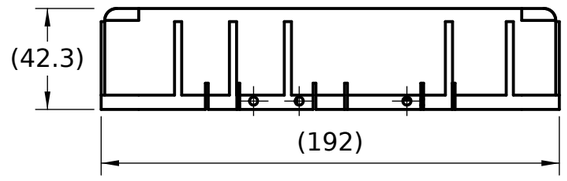

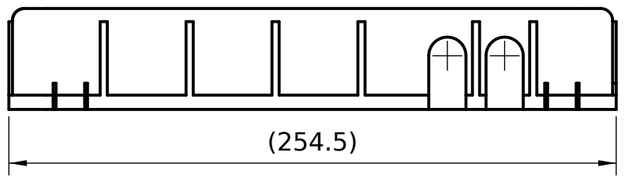

NOTES:

1. PA12, POWDER-BED PRINTED (SLS / MJF). PRINT FROM THE STEP MODEL.
2. SIZES ON THIS SHEET ARE FOR CHECKING ONLY (OVERALL SIZE). THE 3D MODEL DEFINES EVERY OTHER FEATURE.

UNLESS OTHERWISE SPECIFIED:
DIMENSIONS ARE IN MILLIMETERS
TOLERANCES:
X ±0.5 X.X ±0.2
X.XX ±0.05 ANGLES ±0.5°
SURFACE FINISH Ra 3.2 µm
INTERPRET PER ASME Y14.5-2018

COMPANY / PROJECT
ST185 CELICA GT-FOUR - LINK ECU CONVERSION

TITLE
POWER BOX - COVER

PART / DWG NO.	REV	MATERIAL
ST185-FB-103	H	PA12 (SLS / MJF)

SCALE	UNITS	SIZE	SHEET	DATE	DRAWN
1:2.5	mm	B (11x17)	1 OF 1	2026-11-13	DG

SOURCE
C:\projects\active\st185-link-ecu-config\cad\fusebox\rev8\Power_Cover_PA12_printed.step

3RD ANGLE