

REVISIONS			
REV	DESCRIPTION	BY	DATE
A	Initial	Claude	13/10/26
B	#272: CSB3-101 body B, CSB3-102 lid B	Claude	16/10/26
C	#273: CSB3-102 lid C	Claude	16/10/26
D	#274: CSB3-101 body C; first assembly drawing (buildability review 18/10/26)	Claude	16/10/26
E	Nylon M6 tab screws (Essentra 50M060100P030) removed from the assembly and its BOM (Dan's markup 18/10/26, R197)	Claude	18/10/26
F	TE HD34-24-33PE is TE's own model (was an envelope, R184); CSB3-102 lid D	Claude	19/10/26


ITEM	QTY	PART NUMBER	DESCRIPTION	MATERIAL / SPEC
1	1	ST185-CSB3-101	CSB3 ENCLOSURE BODY	6061-T6 AL, MACHINED
2	1	ST185-CSB3-102	CSB3 ENCLOSURE LID	6061-T6 AL, MACHINED
3	1	ECUMASTER CSB3	CAN SWITCH BOARD (CUSTOMER SUPPLIED)	PURCHASED
4	1	TE HD34-24-33PE	HD30 FLANGE RECEPTACLE 33P	PURCHASED
5	1	TE 112263-90	PANEL NUT SIZE 24 (FOR ITEM 4) (NOT SHOWN)	PURCHASED
6	1	TE 112264-ZZ	LOCKWASHER SIZE 24 (FOR ITEM 4) (NOT SHOWN)	PURCHASED
7	26	TE 0460-202-2031	SIZE 20 SOLID PIN (IN ITEM 4) (NOT SHOWN)	PURCHASED
8	2	CAT. 8847 L=10	PCB SUPPORT, NYLON LOCK-IN, L 10	NYLON
9	2	ISO 4026 M8 x 6	FLOOR SEAL SET SCREW, FLAT POINT	A2 STAINLESS
10	1	PARKER N0674-70 2-039	O-RING AS568-039, LID FACE SEAL	NBR 70
11	4	ISO 10642 M3 x 12	LID SCREW, CSK SOCKET HEAD	A2 STAINLESS
12	1	TE HD36-24-33SE	HD30 PLUG 33S (HARNESS SIDE) (NOT SHOWN)	PURCHASED
13	26	TE 0462-201-2031	SIZE 20 SOLID SOCKET (IN ITEM 12) (NOT SHOWN)	PURCHASED
14	7	TE 0413-204-2005	SIZE 20 SEALING PLUG, UNUSED CAVITIES (NOT SHOWN)	PURCHASED

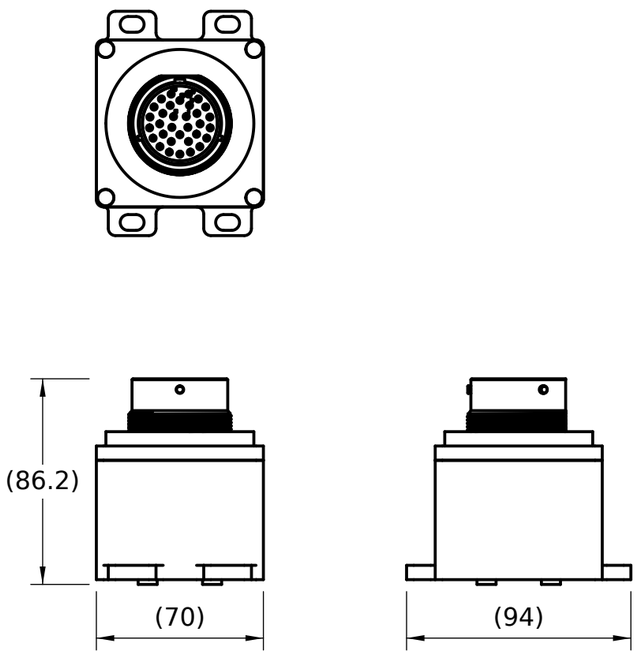

FRONT / TOP / RIGHT VIEWS SCALE 1:2.5

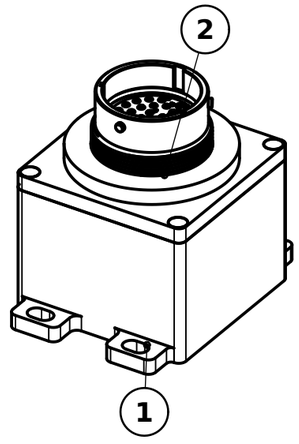

TRIMETRIC VIEW

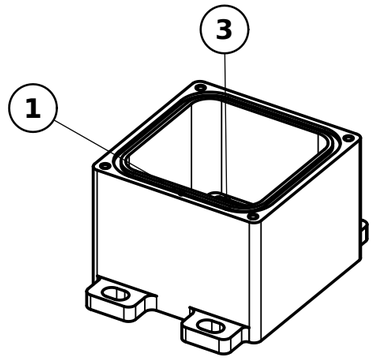

TRIMETRIC - LID REMOVED

NOTES:

1. TIGHTEN THE 4 M3 LID SCREWS A LITTLE AT A TIME, CRISS-CROSS. THE LID SITS METAL TO METAL ON THE RIM.

UNLESS OTHERWISE SPECIFIED:
DIMENSIONS ARE IN MILLIMETERS
TOLERANCES:
X ±0.5 X.X ±0.2
X.XX ±0.05 ANGLES ±0.5°
SURFACE FINISH Ra 3.2 µm
INTERPRET PER ASME Y14.5-2018

COMPANY / PROJECT
ST185 CELICA GT-FOUR - LINK ECU CONVERSION

TITLE
CSB3 ENCLOSURE - ASSEMBLY


PART / DWG NO.	REV	MATERIAL
ST185-CSB3-100	F	SEE BOM

SCALE	UNITS	SIZE	SHEET	DATE	DRAWN
1:2.5	mm	B (11x17)	1 OF 2	2026-10-19	SteveCAD

SOURCE C:\\projects\\active\\st185-link-ecu-config\\cad\\enclosures\\csb3\\CSB3_assembly.step
3RD ANGLE


STEP 1: SET SCREWS FROM BELOW, LOCK-IN SUPPORTS, CSB3 BOARD

EXPLODED TRIMETRIC (NOT TO SCALE)

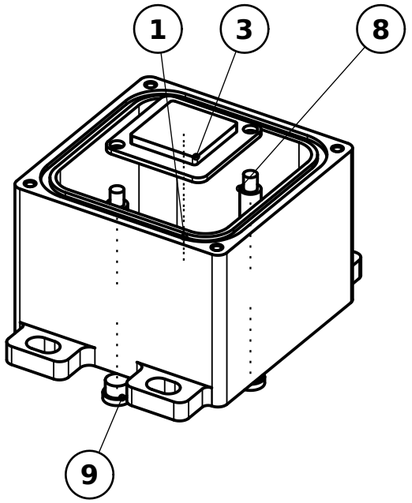


STEP 2: HD34 RECEPTACLE UP INTO THE LID

EXPLODED, SEEN FROM BELOW (NOT TO SCALE)

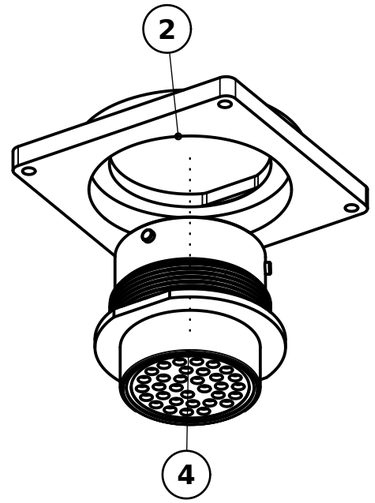

STEP 3: O-RING, LID, LID SCREWS

EXPLODED TRIMETRIC (NOT TO SCALE)

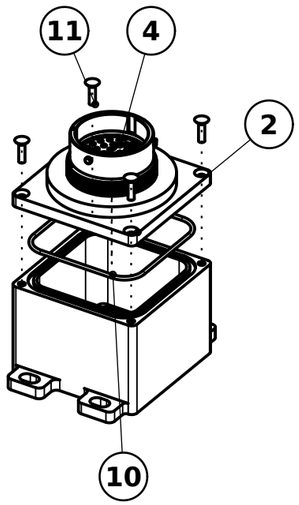

UNLESS OTHERWISE SPECIFIED:
DIMENSIONS ARE IN MILLIMETERS
TOLERANCES:
X ±0.5 X.X ±0.2
X.XX ±0.05 ANGLES ±0.5°
SURFACE FINISH Ra 3.2 µm
INTERPRET PER ASME Y14.5-2018

COMPANY / PROJECT
ST185 CELICA GT-FOUR - LINK ECU CONVERSION

TITLE
CSB3 ENCLOSURE - ASSEMBLY

PART / DWG NO.	REV	MATERIAL
ST185-CSB3-100	**F**	SEE BOM

SCALE	UNITS	SIZE	SHEET	DATE	DRAWN
AS SHOWN	mm	B (11x17)	2 OF 2	2026-10-19	SteveCAD

SOURCE C:\\projects\\active\\st185-link-ecu-config\\cad\\enclosures\\csb3\\CSB3_assembly.step

3RD ANGLE