

REVISIONS			
REV	DESCRIPTION	BY	DATE
B	#272: CSB3-101 body B, CSB3-102 lid B	DG	16/10/26
C	#273: CSB3-102 lid C	DG	16/10/26
D	#274: CSB3-101 body C; first assembly drawing (buildability review 18/10/26)	DG	16/10/26
E	Nylon M6 tab screws (Essentra 50M060100P030) removed from the assembly and its BOM (Dan's markup 18/10/26, R197)	DG	18/10/26
F	TE HD34-24-33PE is TE's own model (was an envelope, R184); CSB3-102 lid D	DG	19/10/26
G	CSB3-101 body D and CSB3-102 lid E: D5 a1 corner ears, SPIROL 150419 inserts, PA12 MJF	DG	09/11/26


ITEM	QTY	PART NUMBER	DESCRIPTION	MATERIAL / SPEC
1	1	ST185-CSB3-101	CSB3 ENCLOSURE BODY	PA12, 3D PRINTED
2	1	ST185-CSB3-102	CSB3 ENCLOSURE LID	PA12, 3D PRINTED
3	1	ECUMASTER CSB3	CAN SWITCH BOARD (CUSTOMER SUPPLIED)	PURCHASED
4	1	TE HD34-24-33PE	HD30 FLANGE RECEPTACLE 33P	PURCHASED
5	1	TE 112263-90	PANEL NUT SIZE 24 (FOR ITEM 4) (NOT SHOWN)	PURCHASED
6	1	TE 112264-ZZ	LOCKWASHER SIZE 24 (FOR ITEM 4) (NOT SHOWN)	PURCHASED
7	26	TE 0460-202-2031	SIZE 20 SOLID PIN (IN ITEM 4) (NOT SHOWN)	PURCHASED
8	2	CAT. 8847 L=10	PCB SUPPORT, NYLON LOCK-IN, L 10	NYLON
9	2	ACCU SSF-M8-6-A2	FLOOR SET SCREW, ISO 4026 M8 x 6 FLAT POINT	A2 STAINLESS
10	1	PARKER N0674-70 2-039	O-RING AS568-039, LID FACE SEAL	NBR 70
11	4	ACCU SSK-M3-12-A2	LID SCREW, ISO 10642 M3 x 12 CSK	A2 STAINLESS
15	4	SPIROL 150419	M3 HEAT-SET INSERT, SERIES 19, IN THE CORNER BORES	BRASS
12	1	TE HD36-24-33SE	HD30 PLUG 33S (HARNESS SIDE) (NOT SHOWN)	PURCHASED
13	26	TE 0462-201-2031	SIZE 20 SOLID SOCKET (IN ITEM 12) (NOT SHOWN)	PURCHASED
14	7	TE 0413-204-2005	SIZE 20 SEALING PLUG, UNUSED CAVITIES (NOT SHOWN)	PURCHASED

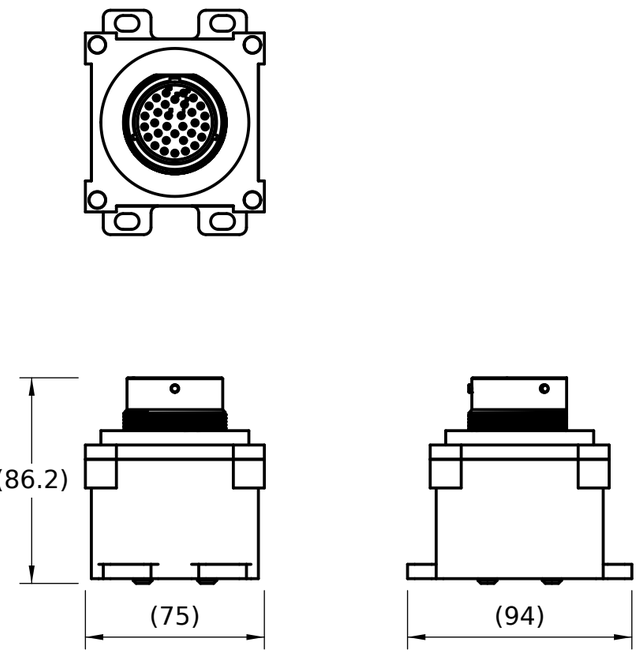

FRONT / TOP / RIGHT VIEWS SCALE 1:2.5

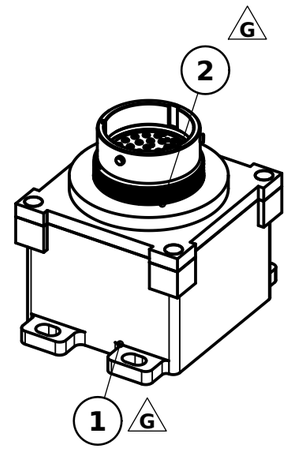

TRIMETRIC VIEW

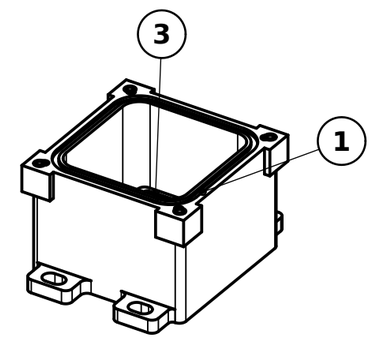

TRIMETRIC - LID REMOVED

NOTES:

1. FIT THE 4 M3 LID SCREWS A LITTLE AT A TIME, CRISS-CROSS. THE LID SITS ON THE PRINTED RIM.

UNLESS OTHERWISE SPECIFIED:
DIMENSIONS ARE IN MILLIMETERS
TOLERANCES:
X ±0.5 X.X ±0.2
X.XX ±0.05 ANGLES ±0.5°
SURFACE FINISH Ra 3.2 µm
INTERPRET PER ASME Y14.5-2018

COMPANY / PROJECT
ST185 CELICA GT-FOUR - LINK ECU CONVERSION

TITLE
CSB3 ENCLOSURE - ASSEMBLY

PART / DWG NO.	REV	MATERIAL
ST185-CSB3-100	G	SEE BOM


SCALE	UNITS	SIZE	SHEET	DATE	DRAWN
1:2.5	mm	B (11x17)	1 OF 2	2026-11-09	DG

SOURCE C:\\projects\\active\\st185-link-ecu-config\\cad\\enclosures\\csb3\\CSB3_assembly.step

3RD ANGLE


STEP 1: SET SCREWS FROM BELOW, LOCK-IN SUPPORTS, CSB3 BOARD

EXPLODED TRIMETRIC (NOT TO SCALE)

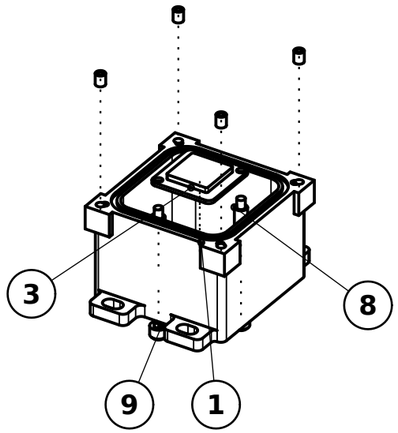


STEP 2: HD34 RECEPTACLE UP INTO THE LID

EXPLODED, SEEN FROM BELOW (NOT TO SCALE)

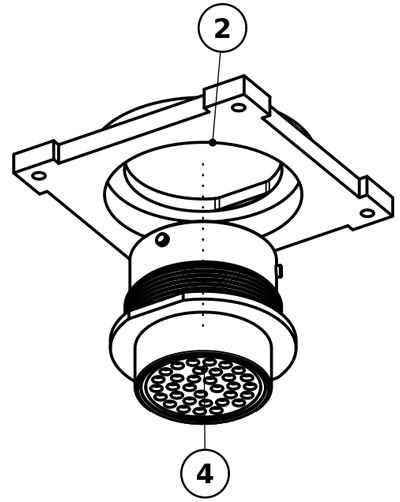

STEP 3: O-RING, LID, LID SCREWS

EXPLODED TRIMETRIC (NOT TO SCALE)

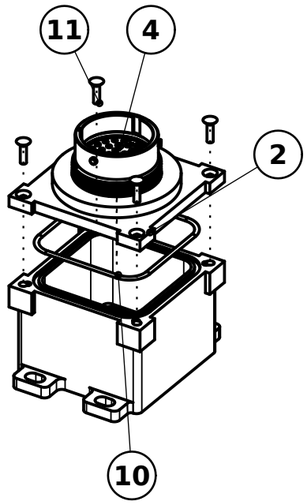

UNLESS OTHERWISE SPECIFIED:
DIMENSIONS ARE IN MILLIMETERS
TOLERANCES:
X ±0.5 X.X ±0.2
X.XX ±0.05 ANGLES ±0.5°
SURFACE FINISH Ra 3.2 µm
INTERPRET PER ASME Y14.5-2018

COMPANY / PROJECT
ST185 CELICA GT-FOUR - LINK ECU CONVERSION

TITLE
CSB3 ENCLOSURE - ASSEMBLY

PART / DWG NO.	REV	MATERIAL
ST185-CSB3-100	**G**	SEE BOM

SCALE	UNITS	SIZE	SHEET	DATE	DRAWN
AS SHOWN	mm	B (11x17)	2 OF 2	2026-11-09	DG

SOURCE C:\\projects\\active\\st185-link-ecu-config\\cad\\enclosures\\csb3\\CSB3_assembly.step

3RD ANGLE