


REVISIONS			
REV	DESCRIPTION	BY	DATE
D	Rev 7 Fusion rebuild with R120-R123 (#265)	DG	15/10/26
E	Wall sweep: every R127 spot fixed or a named exemption (R128) (#270)	DG	16/10/26
F	R127 amendment: outer walls grown outward to 4.3, curved bend saddles back (#271)	DG	16/10/26
G	R146: POWER standoffs hold themselves (crush ribs + LOCTITE 406), R144 collars removed; bar snap tabs (#277); first drawing issued (#280)	DG	17/10/26
H	Dan's markup 17/10/26 (23-06 / R157 / R160): bigger bar tabs, two pad tabs, lug cradles, rim root fillets	DG	18/10/26
J	Fit audit 18/10/26 (R165): copper on the real HCR150 studs (terminal 3 x 128.45, power line y_b − 9.0), pump-lug cradle clear of the 19.1 terminal blocks	DG	18/10/26

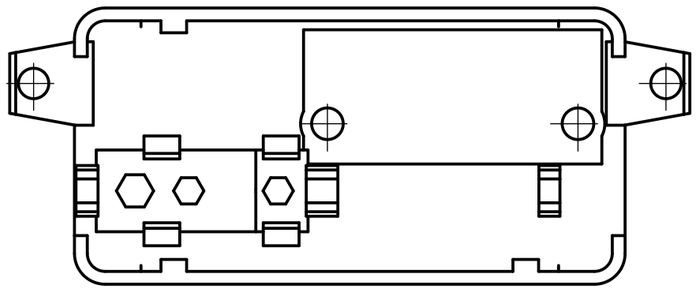

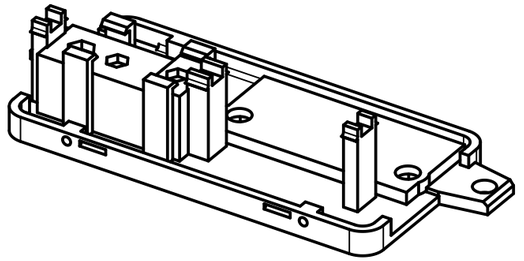

TRIMETRIC VIEW (SCALE 1:2.5)

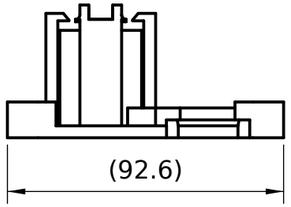



NOTES:

1. PA12, POWDER-BED PRINTED (SLS / MJF). PRINT FROM THE STEP MODEL.
2. SIZES ON THIS SHEET ARE FOR CHECKING ONLY (OVERALL SIZE). THE 3D MODEL DEFINES EVERY OTHER FEATURE.

UNLESS OTHERWISE SPECIFIED:
DIMENSIONS ARE IN MILLIMETERS
TOLERANCES:
X ±0.5 X.X ±0.2
X.XX ±0.05 ANGLES ±0.5°
SURFACE FINISH Ra 3.2 µm
INTERPRET PER ASME Y14.5-2018

COMPANY / PROJECT
ST185 CELICA GT-FOUR - LINK ECU CONVERSION

TITLE
BATTRELAY BOX - BASE

PART / DWG NO.	REV	MATERIAL
ST185-FB-108	**J.02**	PA12 (SLS / MJF)

SCALE	UNITS	SIZE	SHEET	DATE	DRAWN
1:2	mm	B (11x17)	1 OF 1	2026-10-19	DG

SOURCE C:\\projects\\active\\st185-link-ecu-config\\cad\\fusebox\\rev7\\BattRelay_Base_PA12_printed.step

3RD ANGLE