



REVISIONS			
REV	DESCRIPTION	BY	DATE
N	LOGIC Bus 2 x 48.1 corner joint stays solid (sweep fixes) (#275); first drawing issued (#280)	DG	17/10/26
P	Dan's markup 17/10/26 (23-21): spare fuse positions deleted, the rest on a 9.35 grid from y 31.7 (jumpers sized by fuse)	DG	18/10/26
R	Fit audit + N21 18/10/26 (R165, R166): micro relay pattern to TE V23074, sockets 3.2 deep; mini fuse sockets at the real 8.1 pitch with TE MCP 2.8 receptacles; box 3.15 wider; spine 3.0	DG	18/10/26
S	HEAD relays M1 / M2 get the 87a blade slot (R170, #308): model changed after the R drawing; drawing reissued in the buildability review 18/10/26	DG	18/10/26
T	Bus strips held on every side by the base: spine pads against each strip, kerb and top lips on the lug face, front stop pads, a rear snap hook per strip	DG	18/10/26
U	Fuse box rev 8 (Dan A15 b): BUS2-12 seat for 1-968849-1 receptacles, the empty BUS2-12 own-input kerb gap kept	DG	13/11/26

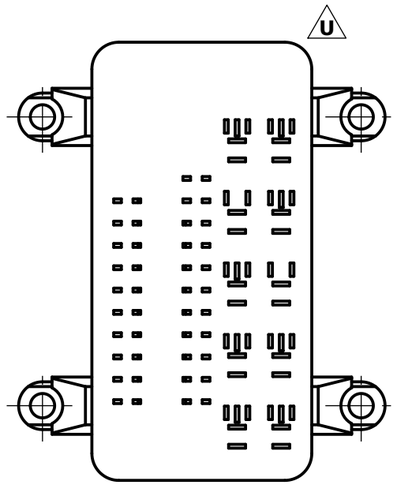

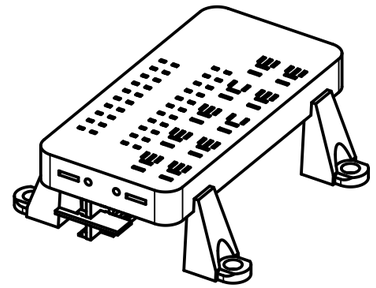

TRIMETRIC VIEW (SCALE 1:3.33)

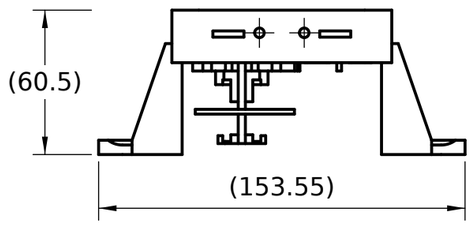

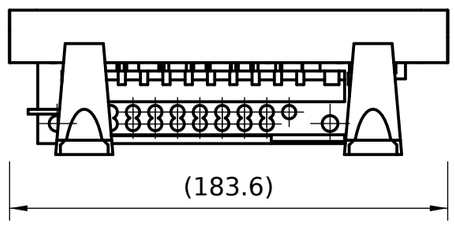

NOTES:

1. PA12, POWDER-BED PRINTED (SLS / MJF). PRINT FROM THE STEP MODEL.
2. SIZES ON THIS SHEET ARE FOR CHECKING ONLY (OVERALL SIZE). THE 3D MODEL DEFINES EVERY OTHER FEATURE.

UNLESS OTHERWISE SPECIFIED:
DIMENSIONS ARE IN MILLIMETERS
TOLERANCES:
X ±0.5 X.X ±0.2
X.XX ±0.05 ANGLES ±0.5°
SURFACE FINISH Ra 3.2 µm
INTERPRET PER ASME Y14.5-2018

COMPANY / PROJECT
ST185 CELICA GT-FOUR - LINK ECU CONVERSION

TITLE
LOGIC BOX - BASE

PART / DWG NO.	REV	MATERIAL
ST185-FB-105	U	PA12 (SLS / MJF)

SCALE	UNITS	SIZE	SHEET	DATE	DRAWN
1:2.5	mm	B (11x17)	1 OF 1	2026-11-13	DG

SOURCE C:\projects\active\st185-link-ecu-config\cad\fusebox\rev8\Logic_Base_PA12_printed.step

3RD ANGLE