



REVISIONS			
REV	DESCRIPTION	BY	DATE
M	SteveCAD audit v3 fixes ported into the source (#272)	Claude	16/10/26
N	Dan's N2 / N3 / N4 answers (#273)	Claude	16/10/26
P	SteveCAD sweep fixes + stud retention collars (R144) (#275)	Claude	17/10/26
R	R146: POWER standoffs hold themselves (crush ribs + LOCTITE 406), R144 collars removed; bar snap tabs (#277); first drawing issued (#280)	Claude; drawing SteveCAD	17/10/26
S	R155 (N14 = B): copper C-strap wells, ledge and snap hooks at all 14 positions; standoff bores, crush ribs and LOCTITE 406 removed	Claude	17/10/26
T	Dan's markup 17/10/26 (R157-R160): hooks bear on the copper (bar catch 2.0, strap arms longer), 6 more bar tabs, lug pockets (POS / NEG), NEG front wall, root fillets, ribs between the strap stations, 5 more cover catches	Claude	18/10/26

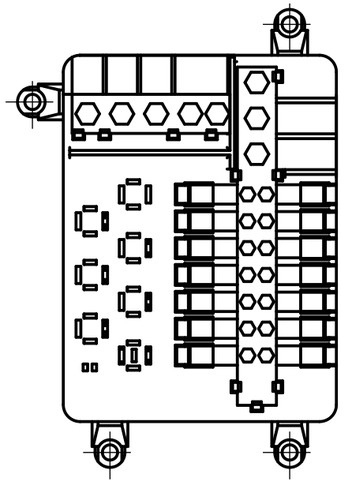

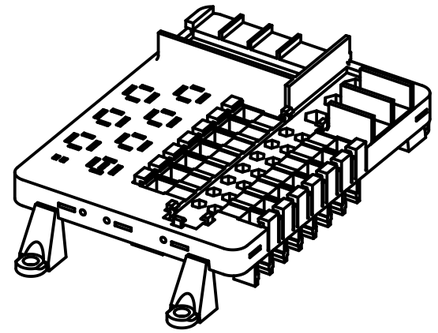

TRIMETRIC VIEW (SCALE 1:4)

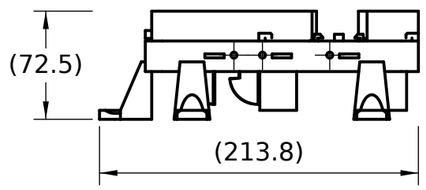

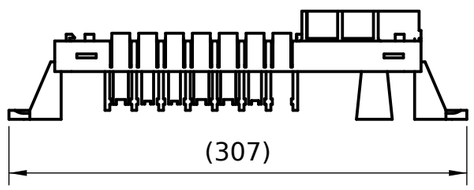

NOTES:

1. MATERIAL: PA12, POWDER-BED PRINTED (SLS/MJF). PRINT FROM THE STL/STEP MODEL.
2. DIMENSIONS ARE REFERENCE ONLY (OVERALL SIZE); THE 3D MODEL DEFINES ALL OTHER FEATURES.
3. VERIFIED 2026-10-17: R145 SLITS FILLED (NO GAP < 0.5, S6).
4. OUTPUTS (R155, N14 = B): 14 WELLS FOR THE COPPER C-STRAPS (ST185-FB-117); THE LIPS REST ON THE LEDGE (DOWN STOP), A SNAP HOOK REACHES OVER THE LIPS (UP STOP) - OUT ROW: THE FREED SKIRT, IN ROW: AN ARM CUT FREE IN THE DECK. NO STANDOFFS, CRUSH RIBS OR ADHESIVE (R146 SUPERSEDED).
5. MARKUP 2026-10-17 (R157 - R160): EVERY HOLD-DOWN HOOK BEARS ON THE COPPER (0 GAP); LUG POCKETS (WALLS + RAISED FLOOR) WHERE EVERY BUS LUG LEAVES THE COPPER; RIBS BETWEEN THE STRAP STATIONS UNDER THE DECK; NEG FRONT WALL; ROOT FILLETS ON THE STANDING WALLS; 7 COVER CATCHES.

UNLESS OTHERWISE SPECIFIED:
DIMENSIONS ARE IN MILLIMETERS
TOLERANCES:
X ±0.5 X.X ±0.2
X.XX ±0.05 ANGLES ±0.5°
BREAK SHARP EDGES 0.2-0.4
SURFACE FINISH Ra 3.2 µm
INTERPRET PER ASME Y14.5-2018

COMPANY / PROJECT
ST185 CELICA GT-FOUR - LINK ECU CONVERSION

TITLE
POWER BOX - BASE

PART / DWG NO.	REV	MATERIAL
ST185-FB-101	T	PA12 (SLS / MJF)

SCALE	UNITS	SIZE	SHEET	DATE	DRAWN
1:4	mm	B (11x17)	1 OF 1	2026-10-18	SteveCAD

SOURCE C:\\projects\\active\\st185-link-ecu-config\\cad\\fusebox\\rev7\\Power_Base_PA12_printed.step

3RD ANGLE