



REVISIONS			
REV	DESCRIPTION	BY	DATE
H	Rev 7 Fusion rebuild with R120-R123 (#265)	Claude	15/10/26
J	Wall sweep: every R127 spot fixed or a named exemption (R128) (#270)	Claude	16/10/26
K	R127 amendment: outer walls grown outward to 4.3, curved bend saddles back (#271)	Claude	16/10/26
M	Dan's N2 / N3 / N4 answers (#273)	Claude	16/10/26
N	LOGIC Bus 2 x 48.1 corner joint stays solid (sweep fixes) (#275); first drawing issued (#280)	Claude; drawing SteveCAD	17/10/26
P	Dan's markup 17/10/26 (23-21): spare fuse positions deleted, the rest on a 9.35 grid from y 31.7 (jumpers sized by fuse)	Claude	18/10/26

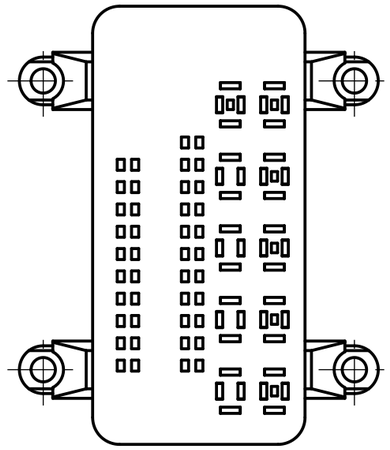

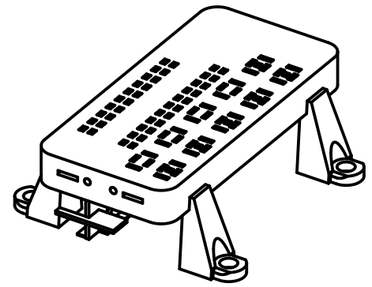

TRIMETRIC VIEW (SCALE 1:3.33)

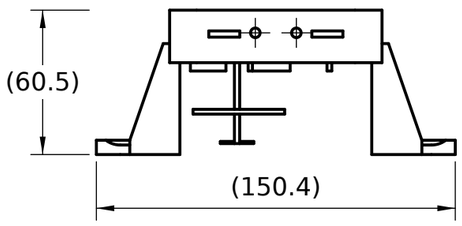

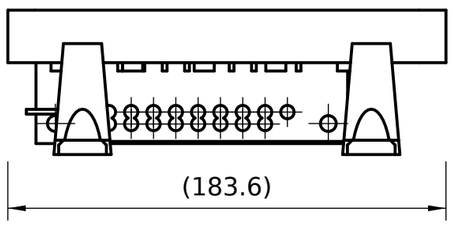

NOTES:

1. MATERIAL: PA12, POWDER-BED PRINTED (SLS/MJF). PRINT FROM THE STL/STEP MODEL.
2. DIMENSIONS ARE REFERENCE ONLY (OVERALL SIZE); THE 3D MODEL DEFINES ALL OTHER FEATURES.

UNLESS OTHERWISE SPECIFIED:
DIMENSIONS ARE IN MILLIMETERS
TOLERANCES:
X ±0.5 X.X ±0.2
X.XX ±0.05 ANGLES ±0.5°
BREAK SHARP EDGES 0.2-0.4
SURFACE FINISH Ra 3.2 µm
INTERPRET PER ASME Y14.5-2018

COMPANY / PROJECT
ST185 CELICA GT-FOUR - LINK ECU CONVERSION

TITLE
LOGIC BOX - BASE

PART / DWG NO.	REV	MATERIAL
ST185-FB-105	**P**	PA12 (SLS / MJF)

SCALE	UNITS	SIZE	SHEET	DATE	DRAWN
1:2.5	mm	B (11x17)	1 OF 1	2026-10-18	SteveCAD

SOURCE C:\\projects\\active\\st185-link-ecu-config\\cad\\fusebox\\rev7\\Logic_Base_PA12_printed.step

3RD ANGLE