REVISIONS			
REV	DESCRIPTION	BY	DATE
A	Initial	Claude	15/10/26
B	Clip leg fix (#266)	Claude	15/10/26
C	R127 amendment: outer walls grown outward to 4.3, curved bend saddles back (#271); first drawing issued (#280)	Claude; drawing SteveCAD	16/10/26
D	Dan's markup 17/10/26 (23-26): wire holes become slots open to the front edge - the clip slides onto the crimped wires	Claude	18/10/26
E	Fit audit 18/10/26 (R165): legs on the hole-zone edge, plate ends + 1.0 (turned R1 30 terminal)	Claude	18/10/26

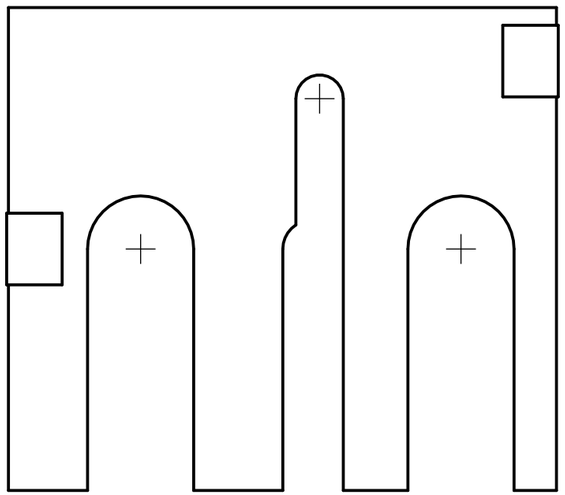

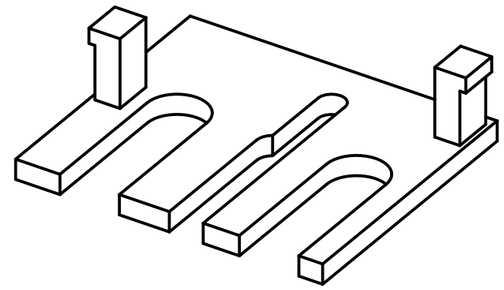

TRIMETRIC VIEW (SCALE 2:1)

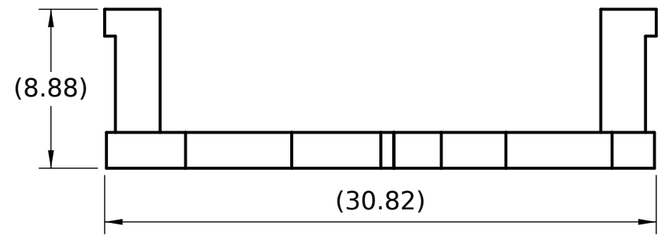

NOTES:

1. MATERIAL: PA12, POWDER-BED PRINTED (SLS/MJF). PRINT FROM THE STL/STEP MODEL.
2. DIMENSIONS ARE REFERENCE ONLY (OVERALL SIZE); THE 3D MODEL DEFINES ALL OTHER FEATURES.

UNLESS OTHERWISE SPECIFIED:
DIMENSIONS ARE IN MILLIMETERS
TOLERANCES:
X ±0.5 X.X ±0.2
X.XX ±0.05 ANGLES ±0.5°
BREAK SHARP EDGES 0.2-0.4
SURFACE FINISH Ra 3.2 µm
INTERPRET PER ASME Y14.5-2018

COMPANY / PROJECT
ST185 CELICA GT-FOUR - LINK ECU CONVERSION

TITLE
R1 RETAINER CLIP

PART / DWG NO.	REV	MATERIAL
ST185-FB-104	**E**	PA12 (SLS / MJF)

SCALE	UNITS	SIZE	SHEET	DATE	DRAWN
3:1	mm	B (11x17)	1 OF 1	2026-10-18	SteveCAD

SOURCE C:\\projects\\active\\st185-link-ecu-config\\cad\\fusebox\\rev7\\ST185_R1_retainer_clip_PA12.step

3RD ANGLE