



REVISIONS			
REV	DESCRIPTION	BY	DATE
R	R146: POWER standoffs hold themselves (crush ribs + LOCTITE 406), R144 collars removed; bar snap tabs (#277); first drawing issued (#280)	Claude; drawing SteveCAD	17/10/26
S	R155 (N14 = B): copper C-strap wells, ledge and snap hooks at all 14 positions; standoff bores, crush ribs and LOCTITE 406 removed	Claude	17/10/26
T	Dan's markup 17/10/26 (R157-R160): hooks bear on the copper (bar catch 2.0, strap arms longer), 6 more bar tabs, lug pockets (POS / NEG), NEG front wall, root fillets, ribs between the strap stations, 5 more cover catches	Claude	18/10/26
U	Fit audit 18/10/26 (R165, R166): relay cavities to the TE drawings (F7 / heater coil line, 30 turned 90 deg), ACPS mini fuse sockets at the real 8.1 pitch (TE MCP 2.8), pan-clearing 30 terminals	Claude	18/10/26
V	Buildability review 18/10/26 (R181): strap hooks get the 40 deg bar-tab lead-in from 0.3 above the underside (the lips cam the hook out; the 0.9 x 45 chamfer left a flat landing). strap seat pocket starts at the bottom-leg end (0.2 -> 0.3 passing clearance)	Claude	18/10/26
W	Strap wells follow the 3.35 longer C-strap bottom leg (N36 = A, R198); under-deck ribs and lug pockets follow the moved lugs	Claude	18/10/26

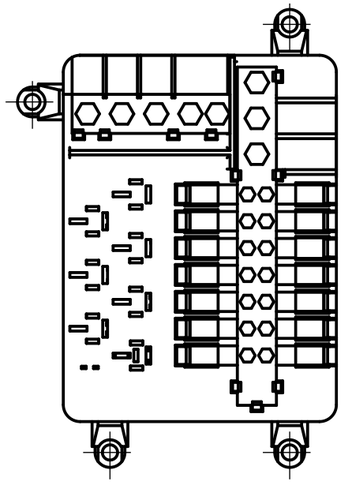

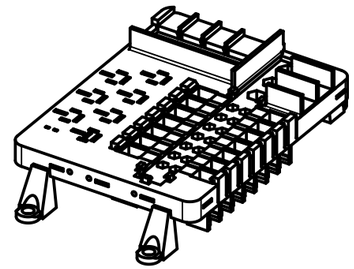

TRIMETRIC VIEW (SCALE 1:5)

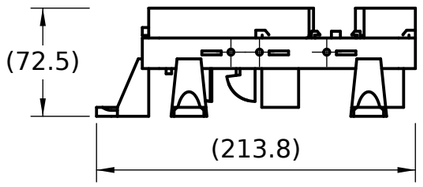

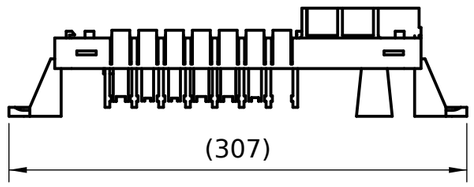

NOTES:

1. PA12, POWDER-BED PRINTED (SLS / MJF). PRINT FROM THE STEP MODEL.
2. SIZES ON THIS SHEET ARE FOR CHECKING ONLY (OVERALL SIZE). THE 3D MODEL DEFINES EVERY OTHER FEATURE.
3. THE 14 WELLS HOLD THE COPPER C-STRAPS (ST185-FB-117): EACH STRAP'S LIPS REST ON THE LEDGE AND A SNAP HOOK CLIPS OVER THEM.

UNLESS OTHERWISE SPECIFIED:
DIMENSIONS ARE IN MILLIMETERS
TOLERANCES:
X ±0.5 X.X ±0.2
X.XX ±0.05 ANGLES ±0.5°
SURFACE FINISH Ra 3.2 µm
INTERPRET PER ASME Y14.5-2018

COMPANY / PROJECT
ST185 CELICA GT-FOUR - LINK ECU CONVERSION

TITLE
POWER BOX - BASE

PART / DWG NO.	REV	MATERIAL
ST185-FB-101	W	PA12 (SLS / MJF)

SCALE	UNITS	SIZE	SHEET	DATE	DRAWN
1:4	mm	B (11x17)	1 OF 1	2026-10-18	SteveCAD

SOURCE C:\\projects\\active\\st185-link-ecu-config\\cad\\fusebox\\rev7\\Power_Base_PA12_printed.step

3RD ANGLE