



REVISIONS			
REV	DESCRIPTION	BY	DATE
C	3 mm wall rule (LOGIC fix) (#215)	Claude	14/10/26
D	J1-J4: crimp-sized holes, guide walls, LOGIC front channel (R94) (#217)	Claude	15/10/26
E	Rev 7 Fusion rebuild with R120-R123 (#265)	Claude	15/10/26
F	Dan's N2 / N3 / N4 answers (#273); first drawing issued (#280)	Claude; drawing SteveCAD	16/10/26
G	Dan's markup 17/10/26 (23-12 / 23-33): two wire-group walls on the pan floor between the harness bundles, root fillets	Claude	18/10/26
H	N21 18/10/26 (R166): 3.15 wider with the LOGIC box; reliefs at the real 86 pins; terminal notches	Claude	18/10/26

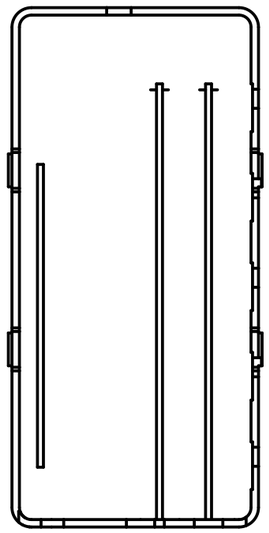

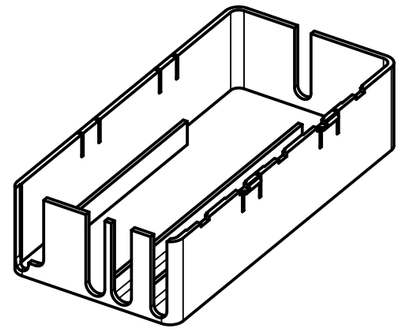

TRIMETRIC VIEW (SCALE 1:2.5)

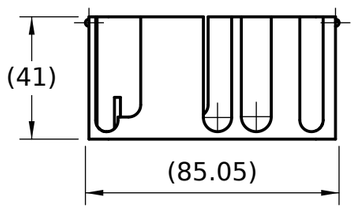

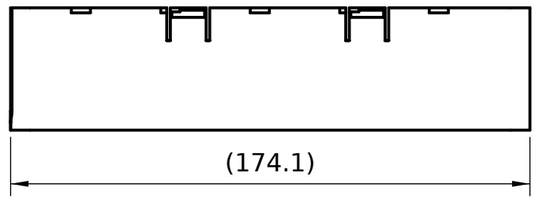

NOTES:

1. PA12, POWDER-BED PRINTED (SLS / MJF). PRINT FROM THE STEP MODEL.
2. SIZES ON THIS SHEET ARE FOR CHECKING ONLY (OVERALL SIZE). THE 3D MODEL DEFINES EVERY OTHER FEATURE.

UNLESS OTHERWISE SPECIFIED:
DIMENSIONS ARE IN MILLIMETERS
TOLERANCES:
X ±0.5 X.X ±0.2
X.XX ±0.05 ANGLES ±0.5°
SURFACE FINISH Ra 3.2 µm
INTERPRET PER ASME Y14.5-2018

COMPANY / PROJECT
ST185 CELICA GT-FOUR - LINK ECU CONVERSION

TITLE
LOGIC BOX - BELLY PAN

PART / DWG NO.	REV	MATERIAL
ST185-FB-106	H.01	PA12 (SLS / MJF)

SCALE	UNITS	SIZE	SHEET	DATE	DRAWN
1:2	mm	B (11x17)	1 OF 1	2026-10-18	SteveCAD

SOURCE C:\\projects\\active\\st185-link-ecu-config\\cad\\fusebox\\rev7\\Logic_Pan_PA12_printed.step

3RD ANGLE