REVISIONS			
REV	DESCRIPTION	BY	DATE
A	Initial	DG	14/10/26
B	SteveCAD audit v3 fixes ported into the source (#272); first drawing issued (#280)	DG	16/10/26
C	Dan's markup 17/10/26 (23-06): battery block pad 25.4 x 3.2 x 15.5 (bar width, from the 1 in x 1/8 in strip stock), held by two snap tabs	DG	18/10/26

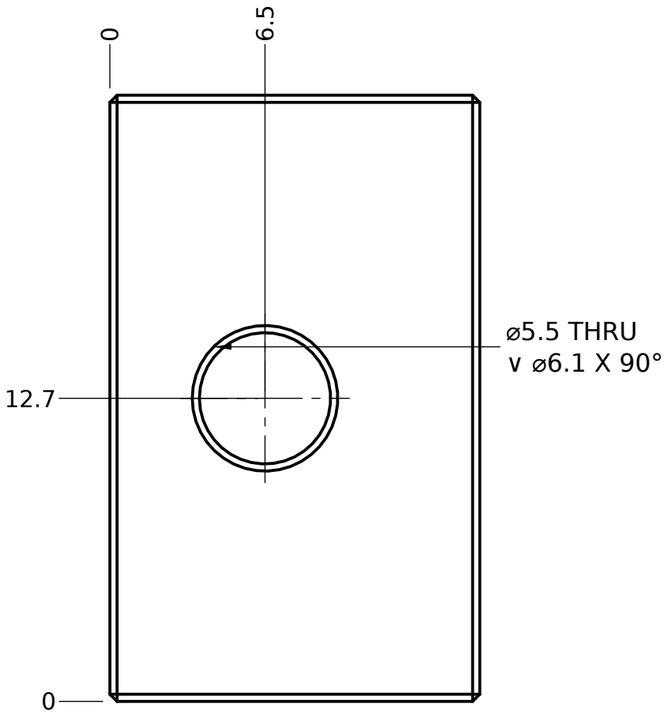

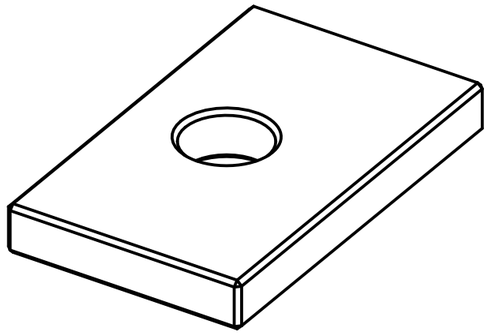

TRIMETRIC VIEW (SCALE 3:1)

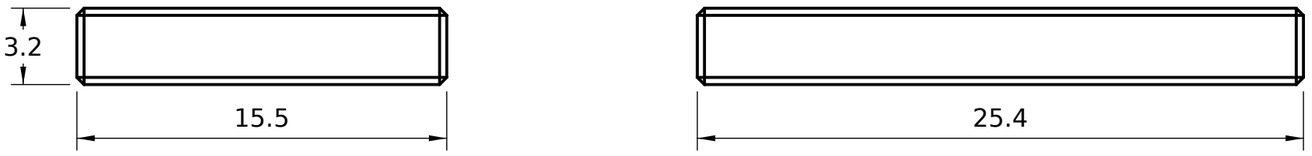

NOTES:

1. C110 COPPER, TINNED. CUT FROM 1" x 1/8" (25.4 x 3.2) TINNED FLAT BAR (MECCANIXITY B0CGJC2S1L, THE SPARE BAR OF THE LOGIC STRIP PAIR). QTY 1.
2. SAW TO LENGTH, DRILL. DEBURR EVERY HOLE AND EDGE. DO NOT REMOVE THE TIN FROM THE CONTACT FACES.

UNLESS OTHERWISE SPECIFIED:
DIMENSIONS ARE IN MILLIMETERS
TOLERANCES:
X ±0.5 X.X ±0.2
X.XX ±0.05 ANGLES ±0.5°
SURFACE FINISH Ra 3.2 µm
INTERPRET PER ASME Y14.5-2018

COMPANY / PROJECT
ST185 CELICA GT-FOUR - LINK ECU CONVERSION

TITLE
BATTERY BLOCK PAD 25.4 x 3.2 x 15.5

PART / DWG NO.	REV	MATERIAL
ST185-FB-112	C.02	C110 COPPER, TINNED

SCALE	UNITS	SIZE	SHEET	DATE	DRAWN
4:1	mm	B (11x17)	1 OF 1	2026-10-19	DG

SOURCE
C:\\projects\\active\\st185-link-ecu-config\\cad\\fusebox\\rev7\\BattRelay_Pad_Out_CuC110_25p4x3p2.step

3RD ANGLE