

REVISIONS			
REV	DESCRIPTION	BY	DATE
E	Fairsolid rev 5: low-profile band clamp saddle	unknown	14/10/26
F	Fairsolid rev 6: flange relief pocket, strut slots, lighter foot	unknown	14/10/26
G	Fairsolid rev 7: bolt-on lug block, strut for the 2 g load	unknown	14/10/26
H	Fairsolid rev 8: lug-block M5 tapped through (rejected)	Claude	17/10/26
J	Flange G: lug integral with the flange (#279)	SteveCAD	17/10/26
K	Option B holder (B9): strut F, foot E, saddle D; first assembly drawing	SteveCAD	17/10/26

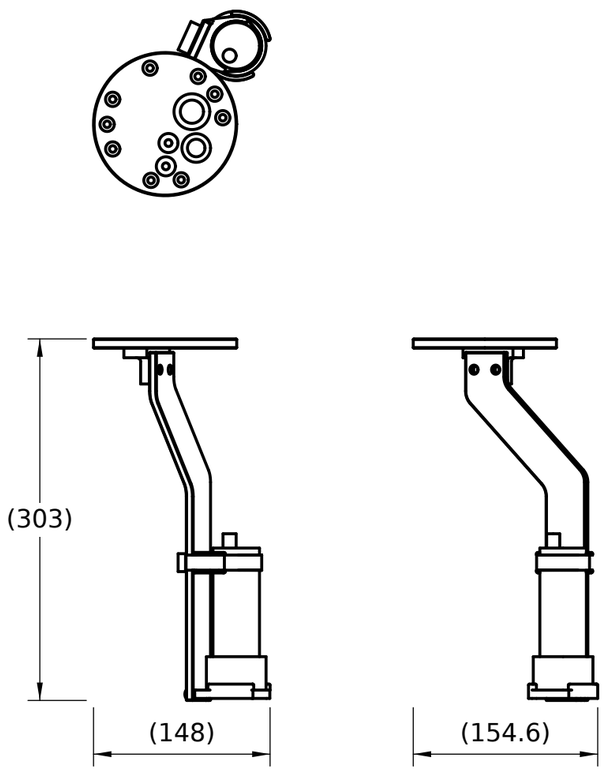

FRONT / TOP / RIGHT VIEWS SCALE 1:5

ITEM	QTY	PART NUMBER	DESCRIPTION	MATERIAL / SPEC
1	1	ST185-FH-101	FUEL HANGER - FLANGE (INTEGRAL LUG)	6061-T6 AL, MACHINED
2	1	ST185-FH-103	FUEL HANGER - STRUT	6061-T6 AL, MACHINED
3	1	ST185-FH-104	FUEL HANGER - FOOT	6061-T6 AL, MACHINED
4	1	ST185-FH-105	FUEL HANGER - PUMP SADDLE	6061-T6 AL, MACHINED
5	2	ISO 10642 M4 x 12	SADDLE SCREW, CSK SOCKET HEAD	A2 STAINLESS
6	2	ISO 4762 M4 x 14	FOOT SCREW, SOCKET HEAD CAP	A2 STAINLESS
7	1	SAE #24 WORM-DRIVE	BAND CLAMP, 12.7 (1/2 IN) BAND	STAINLESS, PURCHASED
8	1	WALBRO F90000295	FUEL PUMP (CUSTOMER SUPPLIED)	PURCHASED
9	2	M6 BOLT + NYLOC NUT	STRUT TO LUG, LENGTH TO SUIT (NOT SHOWN)	A2 STAINLESS

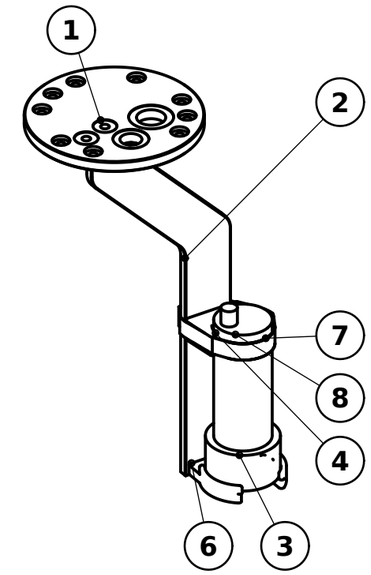

TRIMETRIC VIEW

NOTES:

1. MADE-WITH: build123d (cad/fuel-hanger). SHOWN AS INSTALLED. OVERALL DIMS ONLY (REF). FITTINGS PER FH-101, NOT SHOWN.
2. ORDER: BULKHEAD NUTS, THEN STRUT TO FLANGE LUG (ITEM 9); FOOT (ITEM 3) WITH 2X ITEM 6 + MEDIUM THREADLOCKER; PUMP INTO THE FOOT.
3. SADDLE (ITEM 4): PUSH TOWARD THE STRUT SO THE TAB BEARS ON THE STRUT SIDE FACE, THEN 2X ITEM 5 AT 2 N·m + LOCTITE 243. BAND CLAMP (ITEM 7) IN THE SADDLE CHANNEL.
4. 2 G HAND CHECK, PUMP MASS 0.6 kg ASSUMED: SADDLE HELD BY M4 PRELOAD FRICTION, SF 38 ALONG THE STRUT (NO KEY).

UNLESS OTHERWISE SPECIFIED:
DIMENSIONS ARE IN MILLIMETERS
TOLERANCES:
X ±0.5 X.X ±0.2
X.XX ±0.05 ANGLES ±0.5°
BREAK SHARP EDGES 0.2-0.4
SURFACE FINISH Ra 3.2 µm
INTERPRET PER ASME Y14.5-2018

COMPANY / PROJECT
ST185 CELICA GT-FOUR - LINK ECU CONVERSION

TITLE
FUEL HANGER - ASSEMBLY

PART / DWG NO.	REV	MATERIAL
ST185-FH-100	K	SEE BOM

SCALE	UNITS	SIZE	SHEET	DATE	DRAWN
1:5	mm	B (11x17)	1 OF 1	2026-10-17	SteveCAD

SOURCE: st185-link-ecu-config\cad\fuel-hanger\fuel-hanger-assembly.step

3RD ANGLE